
Distinta di taglio e montaggio

Espositore calze neve su pallet EPAL 1 · quote in cm, fori e viti in mm

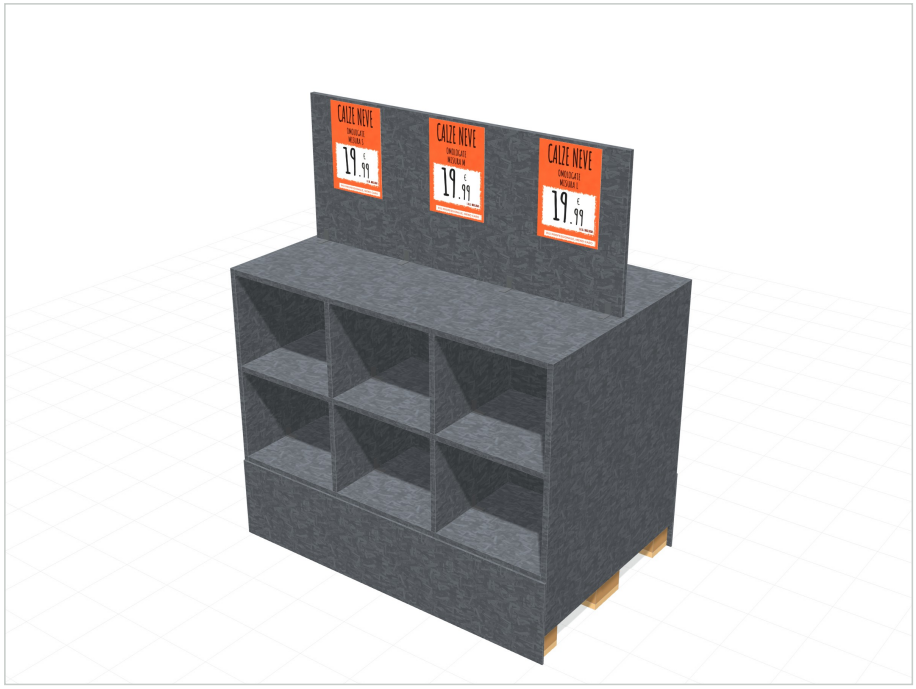

CONFIGURAZIONE

Pallet EPAL 1	**2 × 120 × 80 × 14,4 cm · h 28,8 cm**
Scaffale	**h 70 cm · 2 livelli + piano superiore**
Vani fronte	**6 × 38,8 × 39,1 × h 32,3 cm**
Vani retro	**4 × 59,1 × 39,1 × h 32,3 cm**
Insegna	**120 × 50 cm · 5 cartelli A4**
Ingombro	**123,6 × 81,2 cm · h 148,8 cm da terra**

FERRAMENTA

Squadretta a L 40 × 40 × 20, sp. 2	**83**
Vite truciolare, fondo e fianchi > pallet 4 × 50	**20**
Vite truciolare testa svasata, squadrette 3,5 × 16	**332**
Vite confirmat (foro con punta a gradino 5/7 mm) 7 × 50	**38**
Vite antracite, pannelli 6 mm > blocchi pallet 3,5 × 30	**12**
Cartello prezzo A4 (S, M, L, XL, XXL)	**5**

PANNELLI DA TAGLIARE

Cod.	Pezzo	Q.tà	Dimensioni cm	Sp. cm	Materiale	m² totali	Tavola
A	**Fianco**	**2**	80 × 88,8	1,8	OSB di pioppo 18 mm, verniciato antracite	1,42	2
B	**Fondo**	**1**	120 × 80	1,8	OSB di pioppo 18 mm, verniciato antracite	0,96	3
C	**Ripiano intermedio**	**1**	120 × 80	1,8	OSB di pioppo 18 mm, verniciato antracite	0,96	4
D	**Piano superiore**	**1**	120 × 80	1,8	OSB di pioppo 18 mm, verniciato antracite	0,96	5
E	**Spina centrale**	**2**	120 × 32,3	1,8	OSB di pioppo 18 mm, verniciato antracite	0,78	6
F	**Divisorio**	**6**	39,1 × 32,3	1,8	OSB di pioppo 18 mm, verniciato antracite	0,76	7
G	**Pannello di chiusura lato lungo**	**2**	123,6 × 28,8	0,6	OSB di pioppo 6 mm, verniciato antracite	0,71	8
H	**Pannello insegna**	**1**	120 × 50	1,8	OSB di pioppo 18 mm, verniciato antracite	0,60	9

Totale per materiale (senza sfrido)

OSB di pioppo 18 mm, verniciato antracite	**6,43 m²**
OSB di pioppo 6 mm, verniciato antracite	**0,71 m²**


ESPOSITORE CALZE NEVE

Tavola 1 di 10 · quote in cm, fori e viti in mm


2 pallet EPAL · scaffale 70 cm / 2 livelli · 29/10/2026

A Fianco

80 × 88,8 × 1,8 cm · OSB di pioppo 18 mm, verniciato antracite

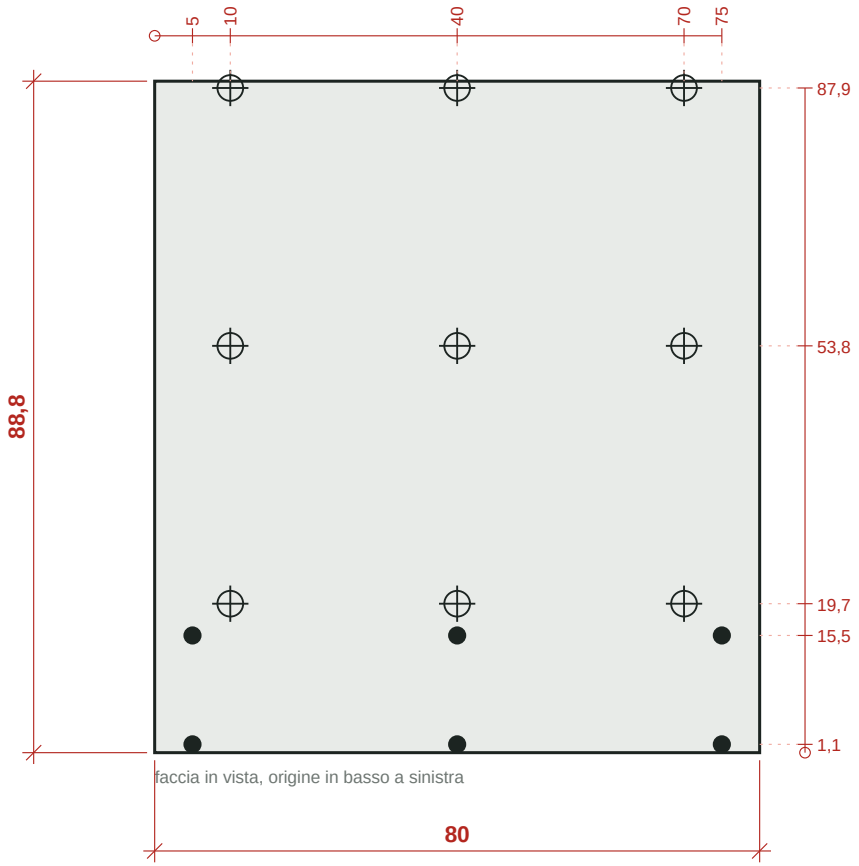

POSIZIONE

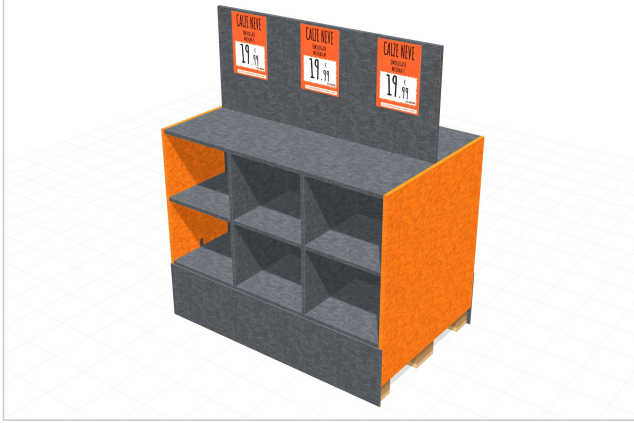

× 2

pezzi uguali da tagliare

Dimensioni	**80 × 88,8 cm**
Spessore	**1,8 cm**
Materiale	**OSB di pioppo 18 mm, verniciato antracite**
Superficie	**0,71 m² cad. · 1,421 m² tot.**

FORI

- 9 × Ø7 passante, svasato · confirmat 7 × 50
- 6 × Ø4 passante, svasato · vite 4 × 50

Fori sulla faccia esterna: confirmat nei bordi di ripiani e piano, viti 4 × 50 nelle traverse dei pallet. Parte da 10 cm da terra, così le aperture per le forche restano libere. Il fianco destro è speculare.


ESPOSITORE CALZE NEVE

Tavola 2 di 10 · scala 1:10 · quote in cm, fori e viti in mm


2 pallet EPAL · scaffale 70 cm / 2 livelli · 29/10/2026

B Fondo

120 × 80 × 1,8 cm · OSB di pioppo 18 mm, verniciato antracite

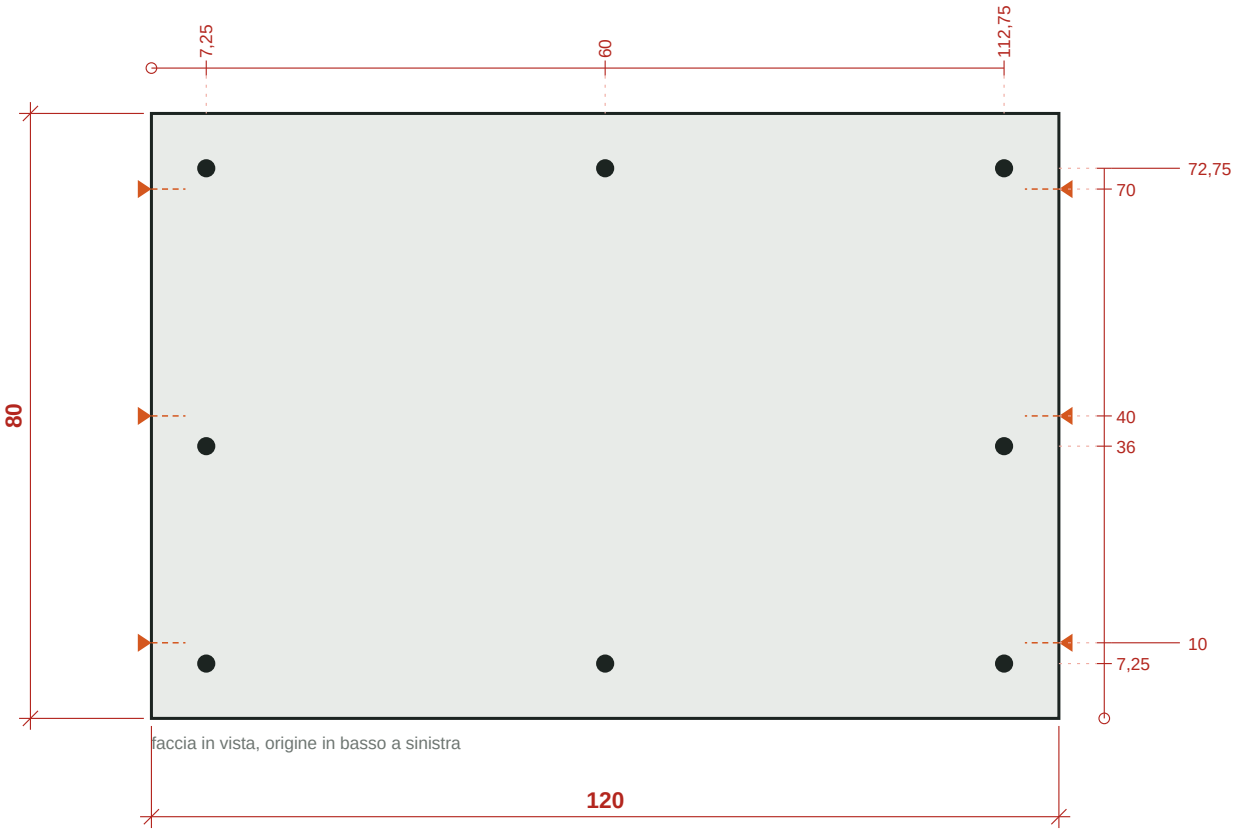

POSIZIONE

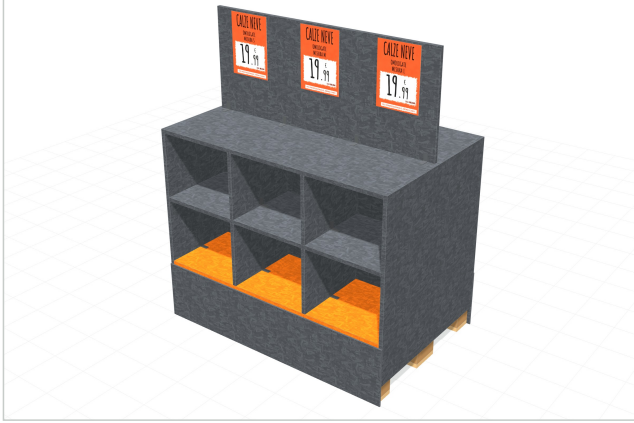

× 1

pezzo da tagliare

Dimensioni	**120 × 80 cm**
Spessore	**1,8 cm**
Materiale	**OSB di pioppo 18 mm, verniciato antracite**
Superficie	**0,96 m² cad. · 0,96 m² tot.**

FORI

- ● 8 × Ø4 passante, svasato · vite 4 × 50
- ▼ 6 × preforo in testa Ø5 prof. 45 · punta del confirmat

Appoggia sul pallet in alto; le viti 4 × 50 entrano nelle tavole del pallet. Sulle teste corte i prefori per i confirmat dei fianchi.

ESPOSITORE CALZE NEVE


Tavola 3 di 10 · scala 1:10 · quote in cm, fori e viti in mm

2 pallet EPAL · scaffale 70 cm / 2 livelli · 29/10/2026


C

Ripiano intermedio

120 × 80 × 1,8 cm · OSB di pioppo 18 mm, verniciato antracite

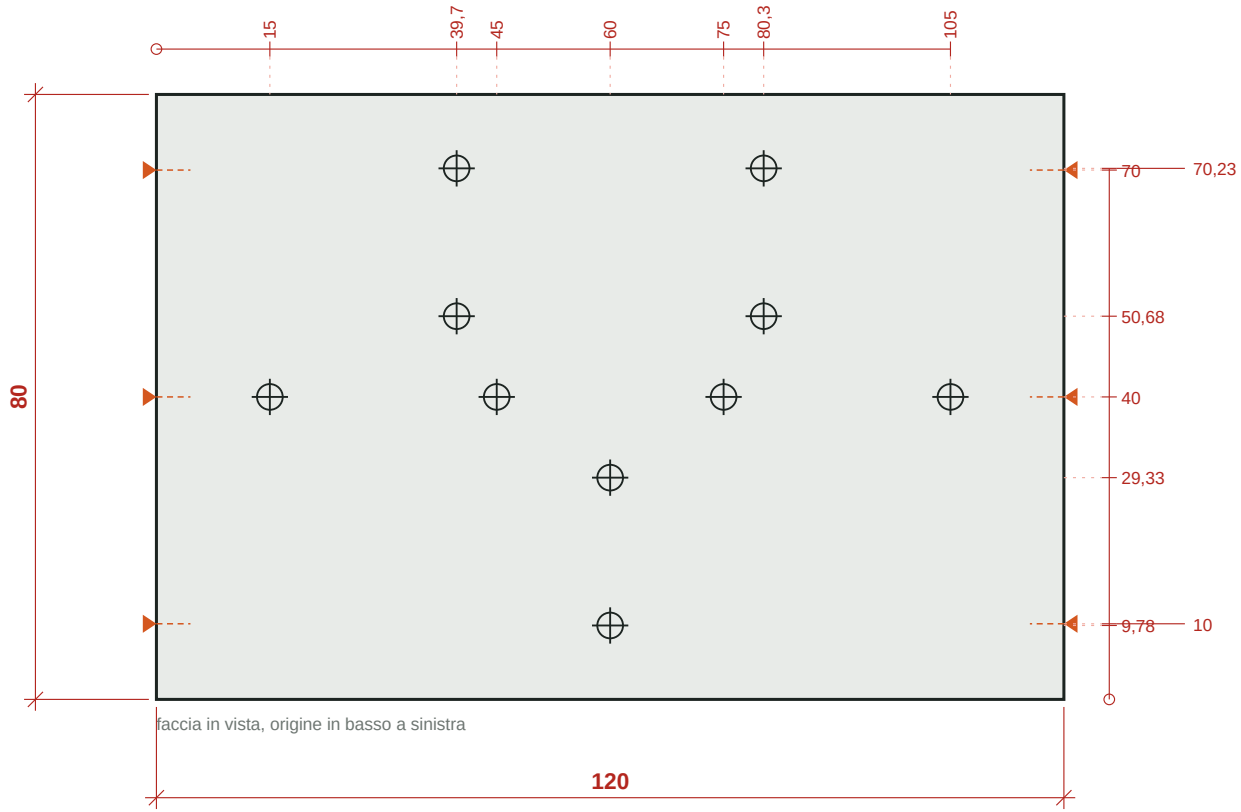

POSIZIONE

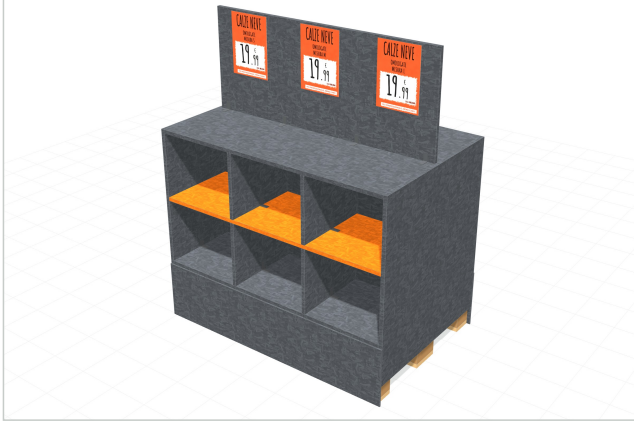

× 1

pezzo da tagliare

Dimensioni	**120 × 80 cm**
Spessore	**1,8 cm**
Materiale	**OSB di pioppo 18 mm, verniciato antracite**
Superficie	**0,96 m² cad. · 0,96 m² tot.**

FORI

⊕ 10 × Ø7 passante, svasato · confirmat 7 × 50

▼ 6 × preforo in testa Ø5 prof. 45 · punta del confirmat

Fori dall'alto per i confirmat nelle teste di spina e divisori del livello sotto. Sulle teste corte i prefori per i confirmat dei fianchi.


ESPOSITORE CALZE NEVE

Tavola 4 di 10 · scala 1:10 · quote in cm, fori e viti in mm


2 pallet EPAL · scaffale 70 cm / 2 livelli · 29/10/2026

D — Piano superiore

120 × 80 × 1,8 cm · OSB di pioppo 18 mm, verniciato antracite

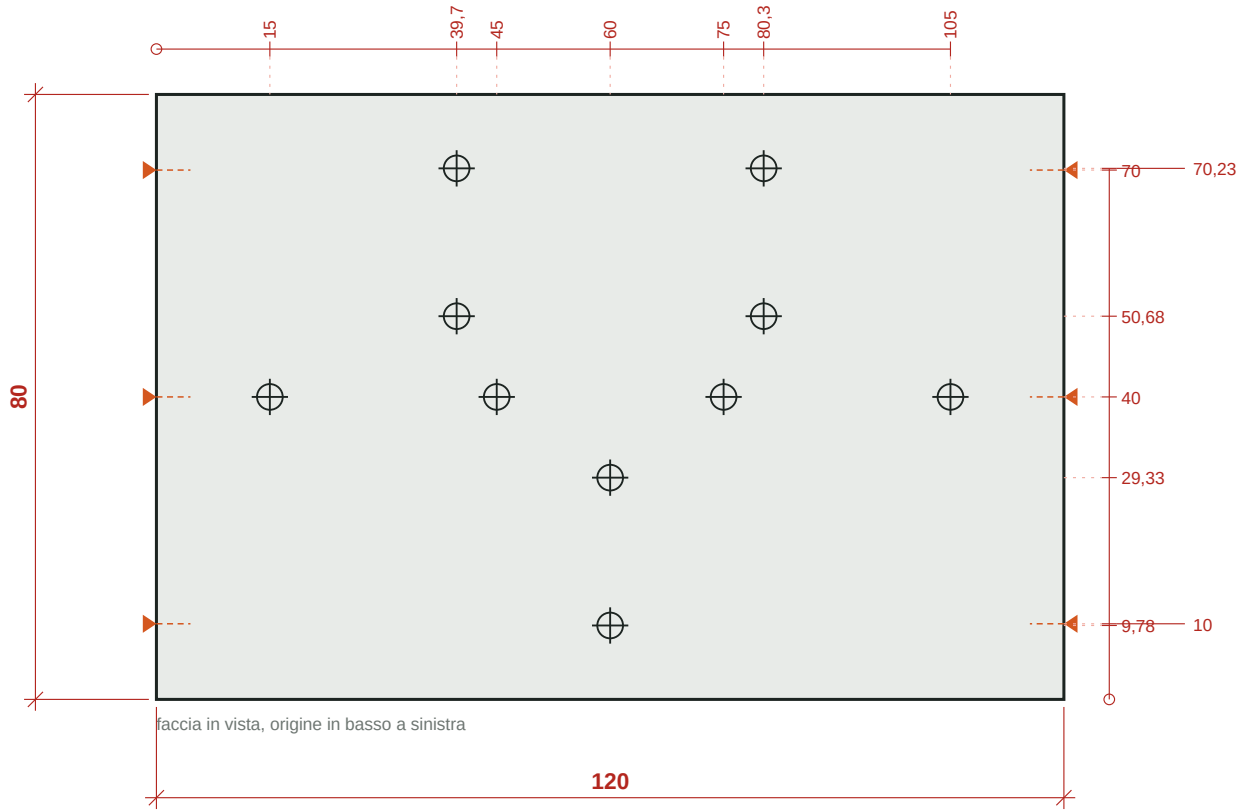

POSIZIONE

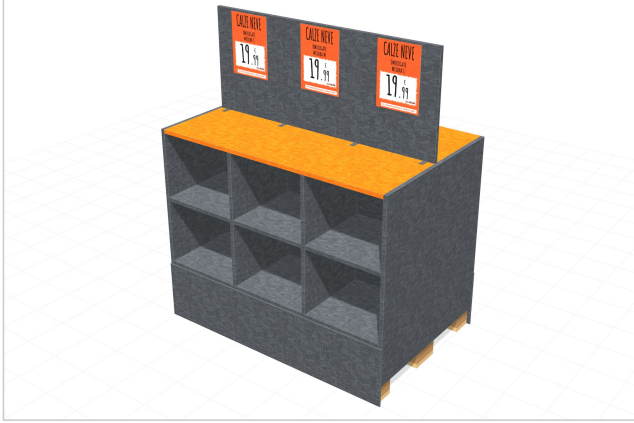

× 1

pezzo da tagliare

Dimensioni	**120 × 80 cm**
Spessore	**1,8 cm**
Materiale	**OSB di pioppo 18 mm, verniciato antracite**
Superficie	**0,96 m² cad. · 0,96 m² tot.**

FORI

- 10 × Ø7 passante, svasato · confirmat 7 × 50
- 6 × preforo in testa Ø5 prof. 45 · punta del confirmat

Come il ripiano intermedio. Sopra, in mezzeria, va in piedi il pannello dell'insegna con le sue squadrette a L.


ESPOSITORE CALZE NEVE

Tavola 5 di 10 · scala 1:10 · quote in cm, fori e viti in mm


2 pallet EPAL · scaffale 70 cm / 2 livelli · 29/10/2026

E Spina centrale

120 × 32,3 × 1,8 cm · OSB di pioppo 18 mm, verniciato antracite

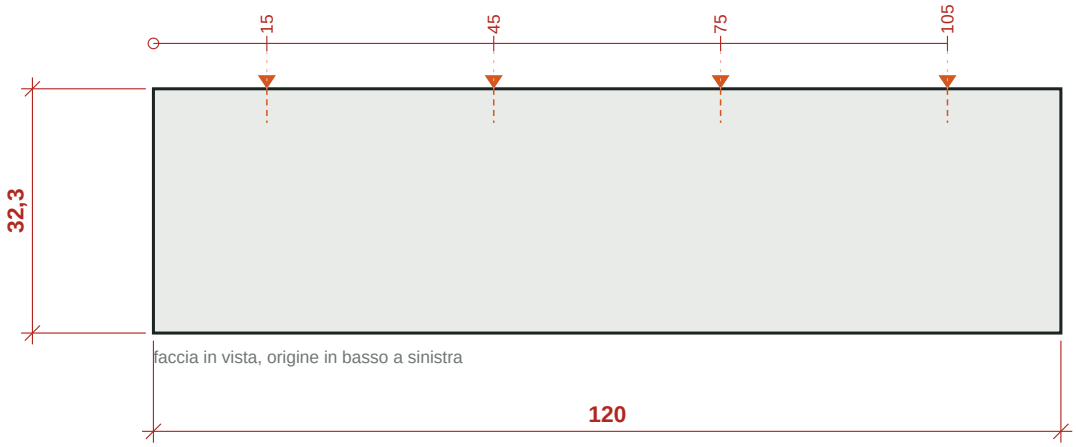

POSIZIONE

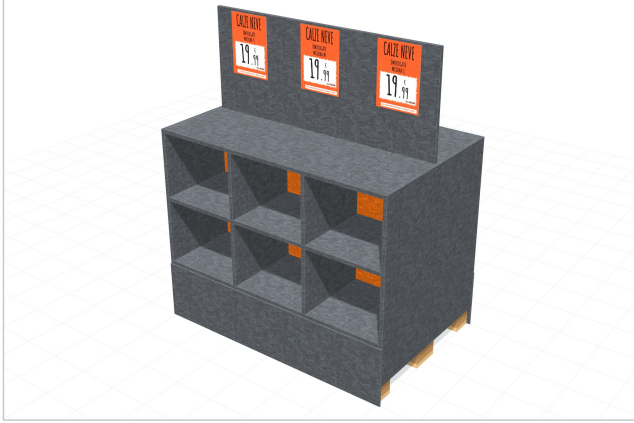

× 2

pezzi uguali da tagliare

Dimensioni	**120 × 32,3 cm**
Spessore	**1,8 cm**
Materiale	**OSB di pioppo 18 mm, verniciato antracite**
Superficie	**0,388 m² cad. · 0,775 m² tot.**

FORI

▼ 4 × preforo in testa Ø5 prof. 45 · punta del confirmat

Testa superiore: prefori per i confirmat del ripiano sopra. Unita al ripiano e ai fianchi con squadrette a L su entrambi i lati.


ESPOSITORE CALZE NEVE

Tavola 6 di 10 · scala 1:10 · quote in cm, fori e viti in mm


2 pallet EPAL · scaffale 70 cm / 2 livelli · 29/10/2026

F — Divisorio

39,1 × 32,3 × 1,8 cm · OSB di pioppo 18 mm, verniciato antracite

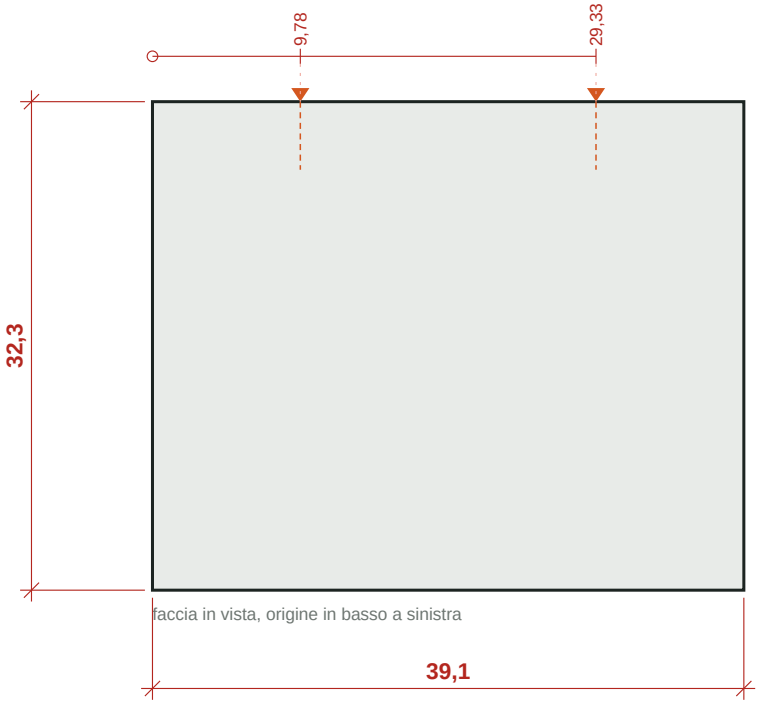

POSIZIONE

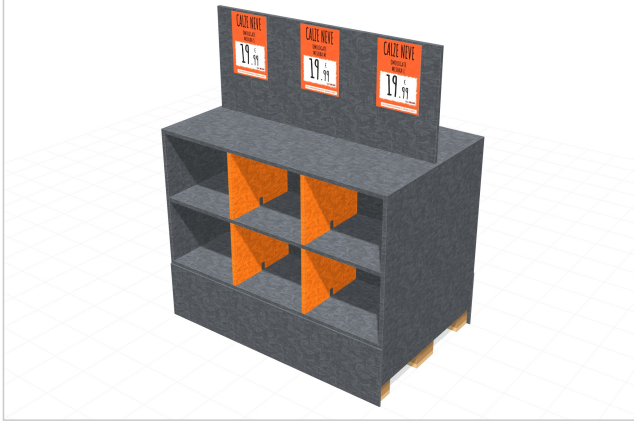

× 6

pezzi uguali da tagliare

Dimensioni	**39,1 × 32,3 cm**
Spessore	**1,8 cm**
Materiale	**OSB di pioppo 18 mm, verniciato antracite**
Superficie	**0,126 m² cad. · 0,758 m² tot.**

FORI

▼ 2 × preforo in testa Ø5 prof. 45 · punta del confirmat

4 sul fronte e 2 sul retro, tutti uguali. Il lato verticale va contro la spina; squadrette al piede, in testa e nell'incrocio a T.

ESPOSITORE CALZE NEVE


Tavola 7 di 10 · scala 1:5 · quote in cm, fori e viti in mm


2 pallet EPAL · scaffale 70 cm / 2 livelli · 29/10/2026

G — Pannello di chiusura lato lungo

123,6 × 28,8 × 0,6 cm · OSB di pioppo 6 mm, verniciato antracite

POSIZIONE

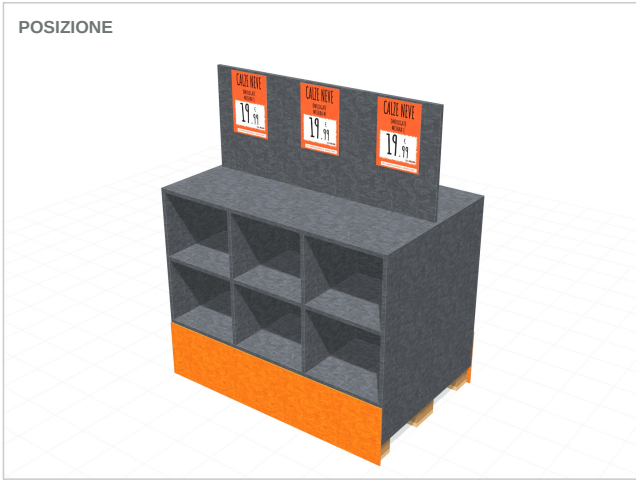

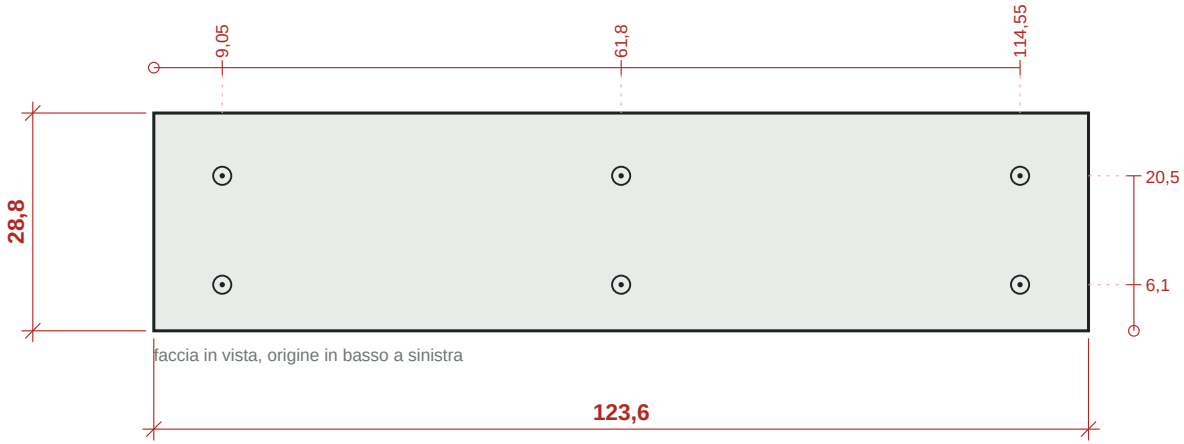

× 2

pezzi uguali da tagliare

Dimensioni	**123,6 × 28,8 cm**
Spessore	**0,6 cm**
Materiale	**OSB di pioppo 6 mm, verniciato antracite**
Superficie	**0,356 m² cad. · 0,712 m² tot.**

FORI

⊙ 6 × Ø3,5 passante, svasato · vite 3,5 × 30

Le viti entrano nei blocchi dei pallet e li legano tra loro. Copre anche i bordi dei fianchi.

ESPOSITORE CALZE NEVE

Tavola 8 di 10 · scala 1:10 · quote in cm, fori e viti in mm

2 pallet EPAL · scaffale 70 cm / 2 livelli · 29/10/2026

H Pannello insegna

120 × 50 × 1,8 cm · OSB di pioppo 18 mm, verniciato antracite

POSIZIONE





× 1

pezzo da tagliare

Dimensioni	**120 × 50 cm**
Spessore	**1,8 cm**
Materiale	**OSB di pioppo 18 mm, verniciato antracite**
Superficie	**0,6 m² cad. · 0,6 m² tot.**

In piedi sul piano superiore, in asse con la spina. Fissato con 7 squadrette a L alla base: sul fronte a 4,5, 39,7, 80,3, 115,5 cm, sul retro a 9,5, 60, 110,5 cm dal bordo sinistro, negli spazi tra i cartelli. I 5 cartelli A4 vanno a 1 cm dal bordo alto, sopra i rispettivi vani.

ESPOSITORE CALZE NEVE

Tavola 9 di 10 · scala 1:10 · quote in cm, fori e viti in mm

2 pallet EPAL · scaffale 70 cm / 2 livelli · 29/10/2026

Sequenza di montaggio

Attrezzi: avvitatore, punta a gradino per confirmat (Ø5/Ø7), punte Ø2,5 e Ø4 con svasatore, metro, squadra, 2 morsetti.

1. Impila i 2 pallet allineati.
2. Appoggia il fondo 1200 × 800 sul pallet in alto e avvitalo alle tavole del pallet. Servono: 8 viti 4 × 50.
3. Livello 1: metti in piedi spina centrale e 3 divisori, fissali al ripiano e tra loro con le squadrette. Servono: 17 squadrette, 68 viti 3,5 × 16.
4. Appoggia il ripiano 2: fissa le squadrette in testa a spina e divisori e avvita dall'alto i confirmat nelle teste. Servono: 11 squadrette, 44 viti 3,5 × 16, 10 confirmat 7 × 50.
5. Livello 2: metti in piedi spina centrale e 3 divisori, fissali al ripiano e tra loro con le squadrette. Servono: 17 squadrette, 68 viti 3,5 × 16.
6. Chiudi con il piano superiore: squadrette in testa a spina e divisori, confirmat dall'alto nelle teste. Servono: 11 squadrette, 44 viti 3,5 × 16, 10 confirmat 7 × 50.
7. Monta i fianchi, fino a 100 da terra: confirmat nei ripiani, viti nelle traverse dei pallet, squadrette negli angoli. Servono: 20 squadrette, 80 viti 3,5 × 16, 18 confirmat 7 × 50, 12 viti 4 × 50.
8. Avvita i pannelli da 6 mm sui lati lunghi, nei blocchi di ogni pallet: coprono i bordi dei fianchi e legano i pallet tra loro. Servono: 12 viti 3,5 × 30.
9. Fissa l'insegna sul piano superiore, in asse con la spina, con le squadrette tra i cartelli. Cartelli A4 a 1 cm dal bordo alto: S, M, L davanti, XL e XXL dietro. Servono: 7 squadrette, 28 viti 3,5 × 16.

Consigli: preforare con punta Ø2,5 tutte le viti delle squadrette per non aprire il bordo del pannello. Montare a vista libera dalla spina verso l'esterno; i fianchi per ultimi tengono in squadra tutto il corpo. Nel configuratore, il montaggio passo-passo mostra ogni vite fuori dal foro con la linea fino al punto d'ingresso.