
# Distinta di taglio e montaggio

Espositore calze neve su pallet EPAL 1 · quote in mm

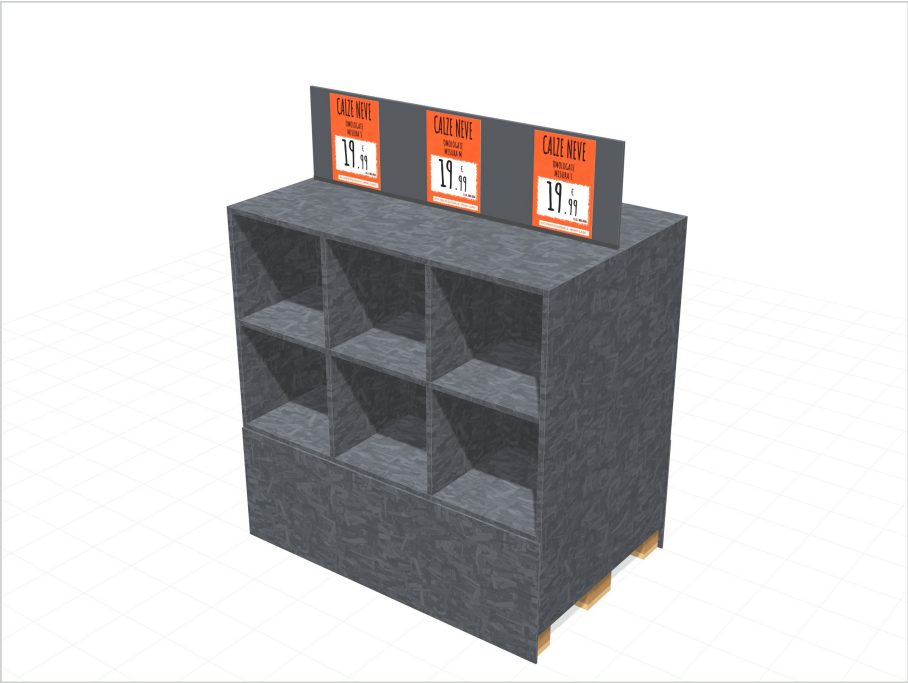


### CONFIGURAZIONE

| | |
|---|---|
| Pallet EPAL 1 | **3 × 1200 × 800 × 144 · h 432** |
| Scaffale | **h 800 · 2 livelli + piano superiore** |
| Vani fronte | **6 × 388 × 391 × h 373** |
| Vani retro | **4 × 591 × 391 × h 373** |
| Insegna | **1200 × 320 · 5 cartelli A4** |
| Ingombro | **1236 × 812 · h 1554 da terra** |

### FERRAMENTA

| | |
|---|---|
| Squadretta a L 40 × 40 × 20, sp. 2 | **76** |
| Vite truciolare, fondo e fianchi > pallet 4 × 50 | **26** |
| Vite truciolare testa svasata, squadrette 3,5 × 16 | **304** |
| Vite confirmat (foro con punta a gradino 5/7 mm) 7 × 50 | **38** |
| Vite antracite, pannelli 6 mm > blocchi pallet 3,5 × 30 | **18** |
| Vite, profilo U > piano superiore 3,5 × 20 | **4** |
| Profilo a U alluminio 1200, luce 10 | **1** |
| Cartello prezzo A4 (S, M, L, XL, XXL) | **5** |

### PANNELLI DA TAGLIARE

| Cod. | Pezzo | Q.tà | Dimensioni | Sp. | Materiale | m² totali | Tavola |
|---|---|---|---|---|---|---|---|
| A | **Fianco** | **2** | 800 × 1132 | 18 | OSB di pioppo 18 mm, verniciato antracite | 1,81 | 2 |
| B | **Fondo** | **1** | 1200 × 800 | 18 | OSB di pioppo 18 mm, verniciato antracite | 0,96 | 3 |
| C | **Ripiano intermedio** | **1** | 1200 × 800 | 18 | OSB di pioppo 18 mm, verniciato antracite | 0,96 | 4 |
| D | **Piano superiore** | **1** | 1200 × 800 | 18 | OSB di pioppo 18 mm, verniciato antracite | 0,96 | 5 |
| E | **Spina centrale** | **2** | 1200 × 373 | 18 | OSB di pioppo 18 mm, verniciato antracite | 0,90 | 6 |
| F | **Divisorio** | **6** | 391 × 373 | 18 | OSB di pioppo 18 mm, verniciato antracite | 0,88 | 7 |
| G | **Pannello di chiusura lato lungo** | **2** | 1236 × 432 | 6 | OSB di pioppo 6 mm, verniciato antracite | 1,07 | 8 |
| H | **Foglio insegna** | **1** | 1200 × 320 | 10 | Forex 10 mm grigio antracite | 0,38 | 9 |

**Totale per materiale (senza sfrido)**

| | |
|---|---|
| OSB di pioppo 18 mm, verniciato antracite | **6,46 m²** |
| OSB di pioppo 6 mm, verniciato antracite | **1,07 m²** |
| Forex 10 mm grigio antracite | **0,38 m²** |


**ESPOSITORE CALZE NEVE**

Tavola 1 di 10 · quote in mm


3 pallet EPAL · scaffale 800 / 2 livelli · 29/10/2026

# A Fianco

800 × 1132 × 18 mm · OSB di pioppo 18 mm, verniciato antracite

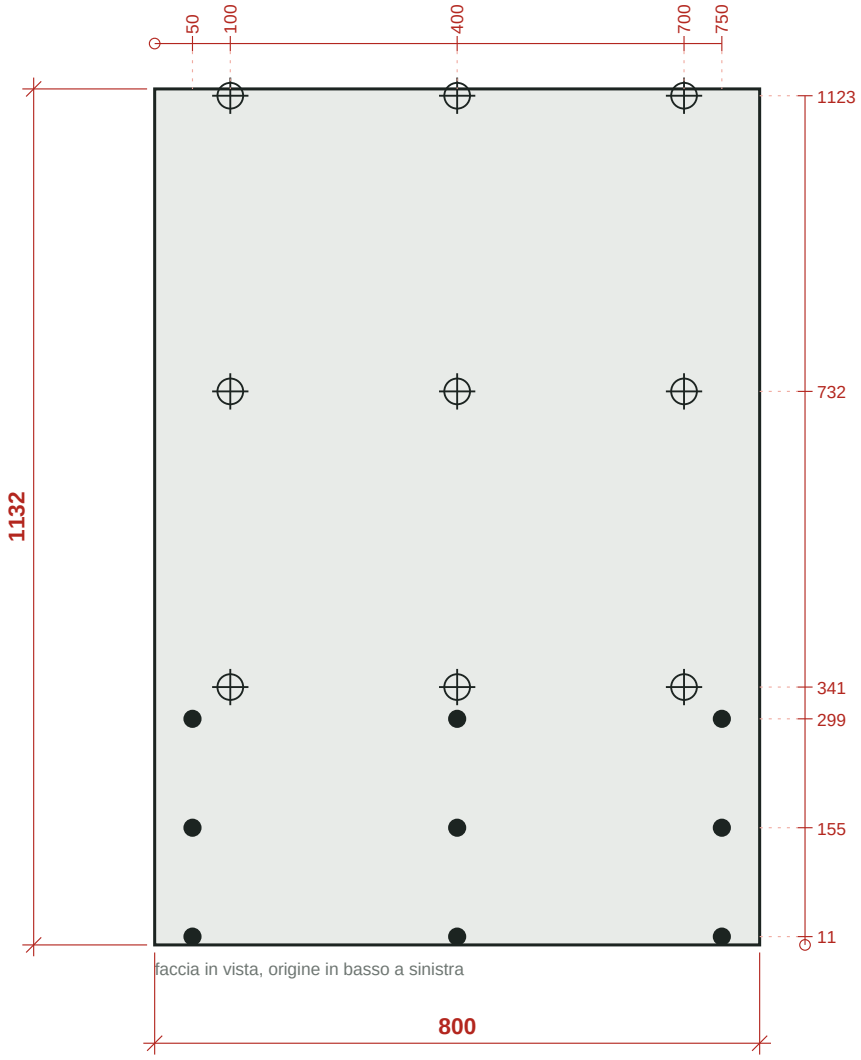


POSIZIONE

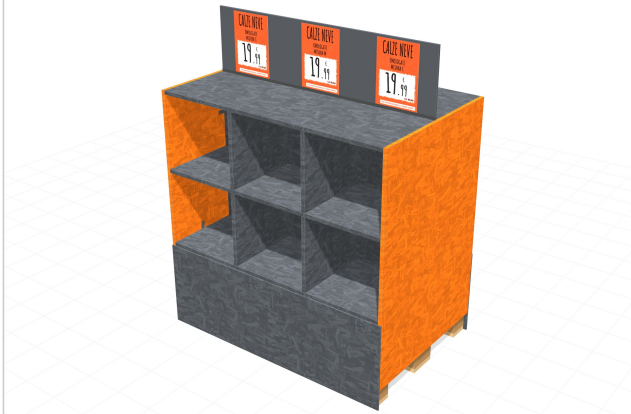


## × 2

pezzi uguali da tagliare

| | |
|---|---|
| Dimensioni | **800 × 1132 mm** |
| Spessore | **18 mm** |
| Materiale | **OSB di pioppo 18 mm, verniciato antracite** |
| Superficie | **0,906 m² cad. · 1,811 m² tot.** |

**FORI**

- 9 × Ø7 passante, svasato · confirmat 7 × 50
- 9 × Ø4 passante, svasato · vite 4 × 50

Fori sulla faccia esterna: confirmat nei bordi di ripiani e piano, viti 4 × 50 nelle traverse dei pallet. Parte da 100 mm da terra, così le aperture per le forche restano libere. Il fianco destro è speculare.


**ESPOSITORE CALZE NEVE**

Tavola 2 di 10 · scala 1:10 · quote in mm


3 pallet EPAL · scaffale 800 / 2 livelli · 29/10/2026

# B Fondo

1200 × 800 × 18 mm · OSB di pioppo 18 mm, verniciato antracite

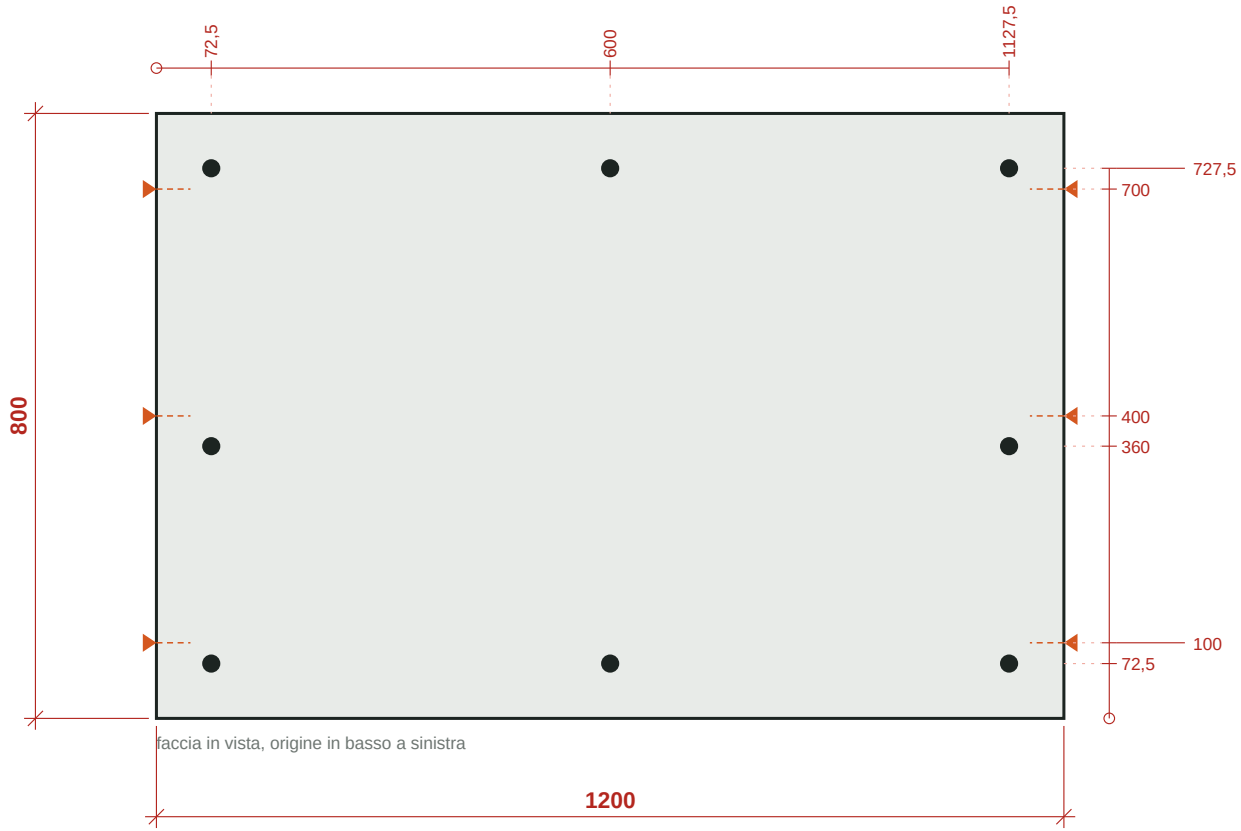


POSIZIONE

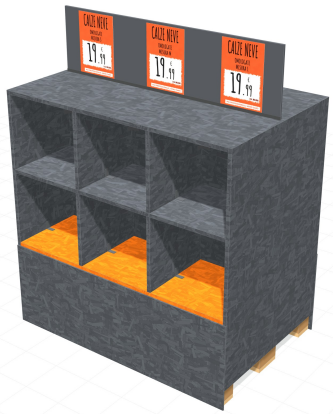

## × 1

pezzo da tagliare

| | |
|---|---|
| Dimensioni | **1200 × 800 mm** |
| Spessore | **18 mm** |
| Materiale | **OSB di pioppo 18 mm, verniciato antracite** |
| Superficie | **0,96 m² cad. · 0,96 m² tot.** |

**FORI**

- ● 8 × Ø4 passante, svasato · vite 4 × 50
- ▼ 6 × preforo in testa Ø5 prof. 45 · punta del confirmat

Appoggia sul pallet in alto; le viti 4 × 50 entrano nelle tavole del pallet. Sulle teste corte i prefori per i confirmat dei fianchi.


**ESPOSITORE CALZE NEVE**

Tavola 3 di 10 · scala 1:10 · quote in mm


3 pallet EPAL · scaffale 800 / 2 livelli · 29/10/2026

# C — Ripiano intermedio

1200 × 800 × 18 mm · OSB di pioppo 18 mm, verniciato antracite

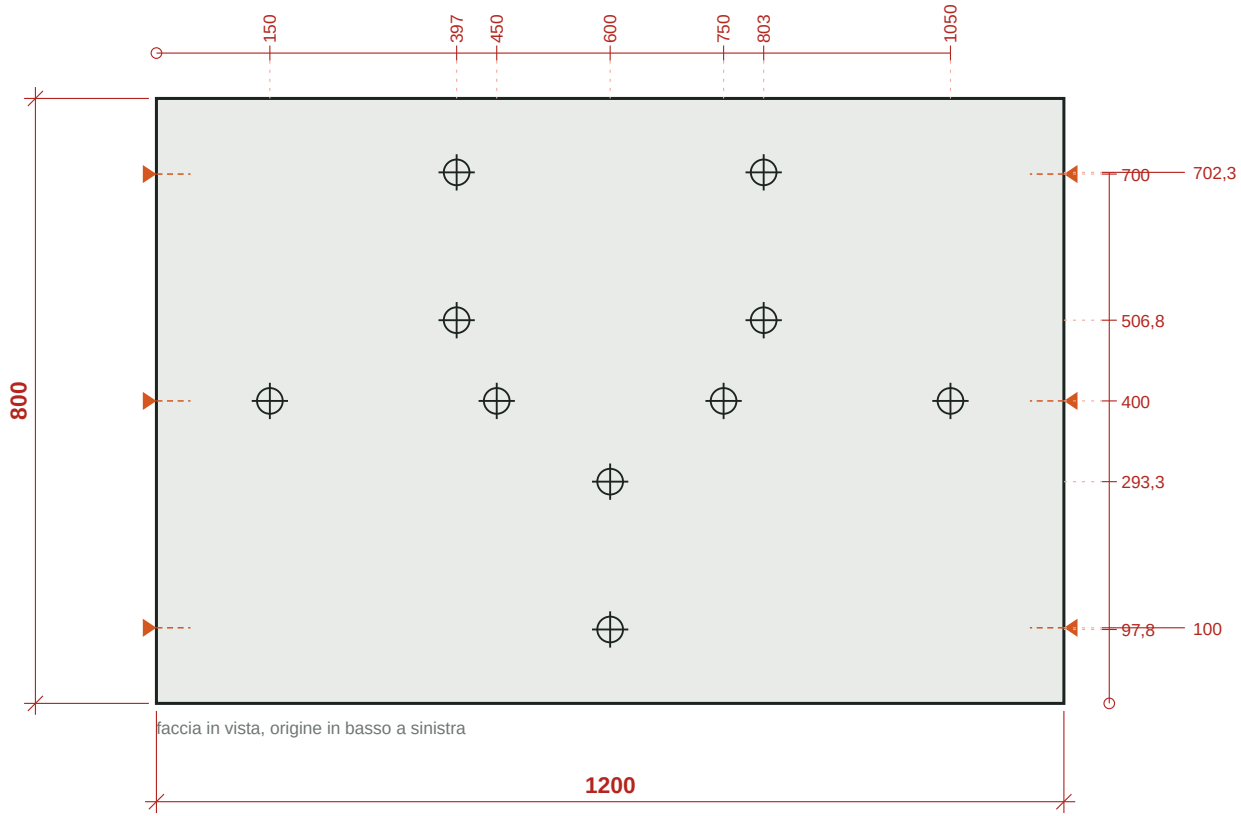


**POSIZIONE**

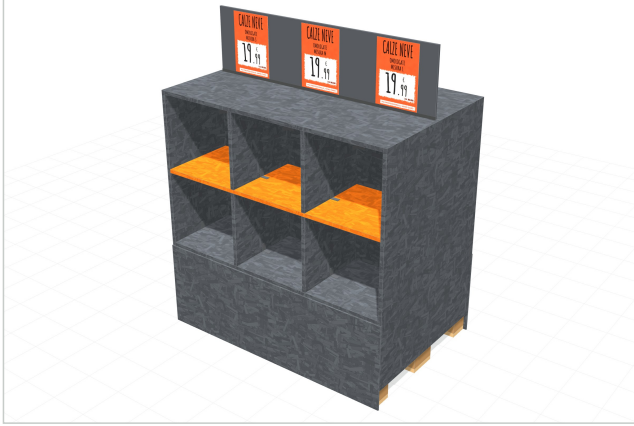

## × 1

pezzo da tagliare

| | |
|---|---|
| Dimensioni | **1200 × 800 mm** |
| Spessore | **18 mm** |
| Materiale | **OSB di pioppo 18 mm, verniciato antracite** |
| Superficie | **0,96 m² cad. · 0,96 m² tot.** |

**FORI**

- 10 × Ø7 passante, svasato · confirmat 7 × 50
- 6 × preforo in testa Ø5 prof. 45 · punta del confirmat

Fori dall'alto per i confirmat nelle teste di spina e divisori del livello sotto. Sulle teste corte i prefori per i confirmat dei fianchi.


**ESPOSITORE CALZE NEVE**

Tavola 4 di 10 · scala 1:10 · quote in mm


3 pallet EPAL · scaffale 800 / 2 livelli · 29/10/2026

# D — Piano superiore

1200 × 800 × 18 mm · OSB di pioppo 18 mm, verniciato antracite

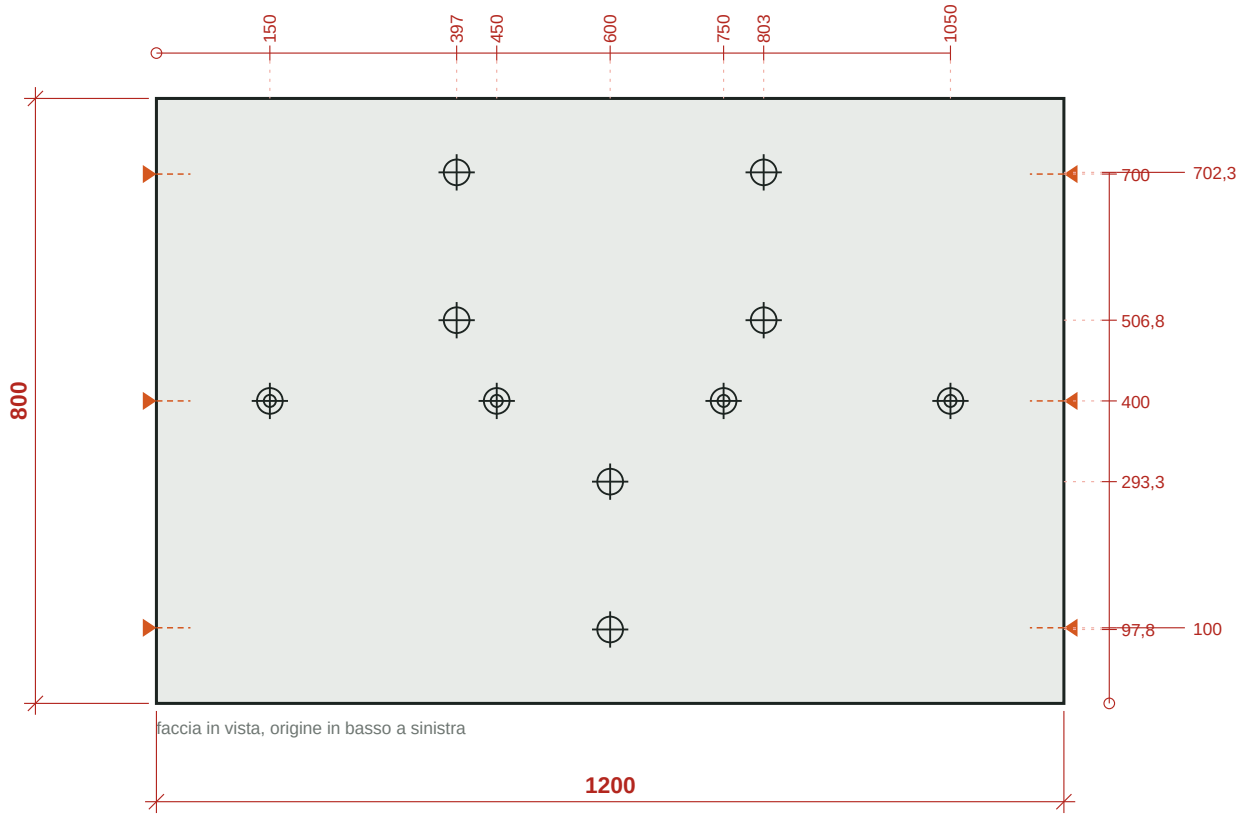


**POSIZIONE**

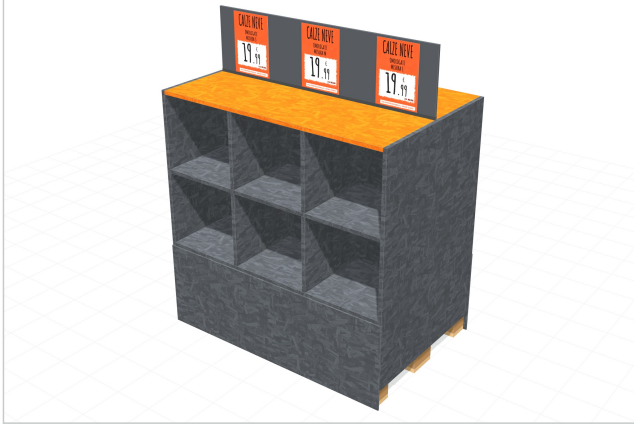

## × 1

pezzo da tagliare

| | |
|---|---|
| Dimensioni | **1200 × 800 mm** |
| Spessore | **18 mm** |
| Materiale | **OSB di pioppo 18 mm, verniciato antracite** |
| Superficie | **0,96 m² cad. · 0,96 m² tot.** |

**FORI**

- ⊕ 10 × Ø7 passante, svasato · confirmat 7 × 50
- ○ 4 × preforo Ø2,5 prof. 15 · vite 3,5 × 20 (profilo U)
- ▼ 6 × preforo in testa Ø5 prof. 45 · punta del confirmat

Come il ripiano intermedio, più 4 prefori in mezzeria per il profilo a U dell'insegna.


**ESPOSITORE CALZE NEVE**

Tavola 5 di 10 · scala 1:10 · quote in mm


3 pallet EPAL · scaffale 800 / 2 livelli · 29/10/2026

# E Spina centrale

1200 × 373 × 18 mm · OSB di pioppo 18 mm, verniciato antracite

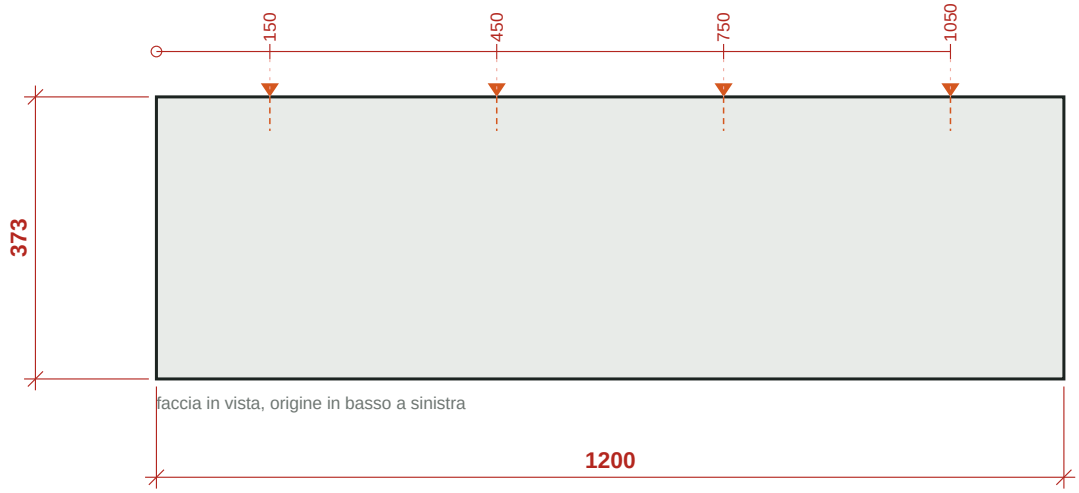


POSIZIONE

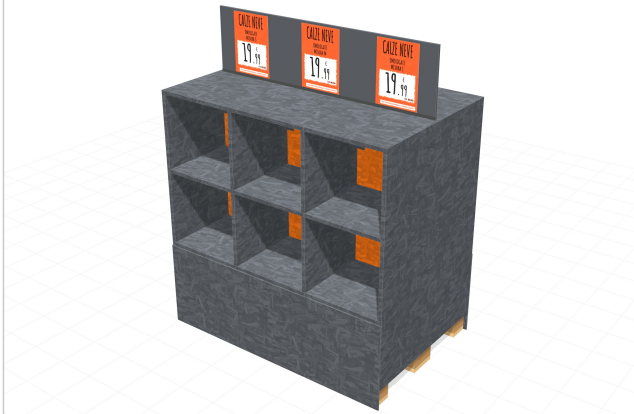

## × 2

pezzi uguali da tagliare

| | |
|---|---|
| Dimensioni | **1200 × 373 mm** |
| Spessore | **18 mm** |
| Materiale | **OSB di pioppo 18 mm, verniciato antracite** |
| Superficie | **0,448 m² cad. · 0,895 m² tot.** |

**FORI**

▼ 4 × preforo in testa Ø5 prof. 45 · punta del confirmat

Testa superiore: prefori per i confirmat del ripiano sopra. Unita al ripiano e ai fianchi con squadrette a L su entrambi i lati.


**ESPOSITORE CALZE NEVE**

Tavola 6 di 10 · scala 1:10 · quote in mm


3 pallet EPAL · scaffale 800 / 2 livelli · 29/10/2026

# F — Divisorio

391 × 373 × 18 mm · OSB di pioppo 18 mm, verniciato antracite

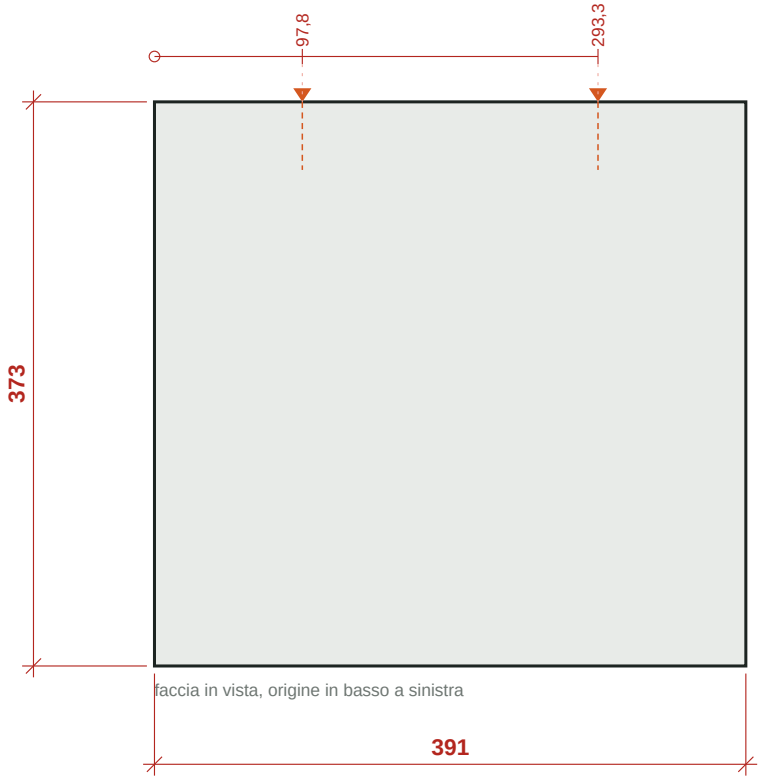


POSIZIONE

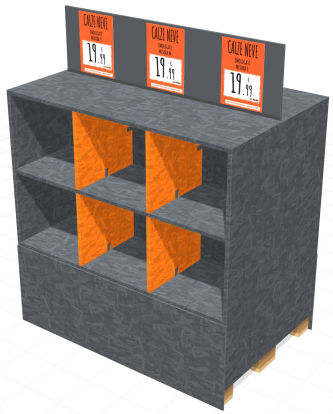


## × 6

pezzi uguali da tagliare

| | |
|---|---|
| Dimensioni | **391 × 373 mm** |
| Spessore | **18 mm** |
| Materiale | **OSB di pioppo 18 mm, verniciato antracite** |
| Superficie | **0,146 m² cad. · 0,875 m² tot.** |

**FORI**

▼ 2 × preforo in testa Ø5 prof. 45 · punta del confirmat

4 sul fronte e 2 sul retro, tutti uguali. Il lato verticale va contro la spina; squadrette al piede, in testa e nell'incrocio a T.


**ESPOSITORE CALZE NEVE**

Tavola 7 di 10 · scala 1:5 · quote in mm


3 pallet EPAL · scaffale 800 / 2 livelli · 29/10/2026

# G — Pannello di chiusura lato lungo

1236 × 432 × 6 mm · OSB di pioppo 6 mm, verniciato antracite

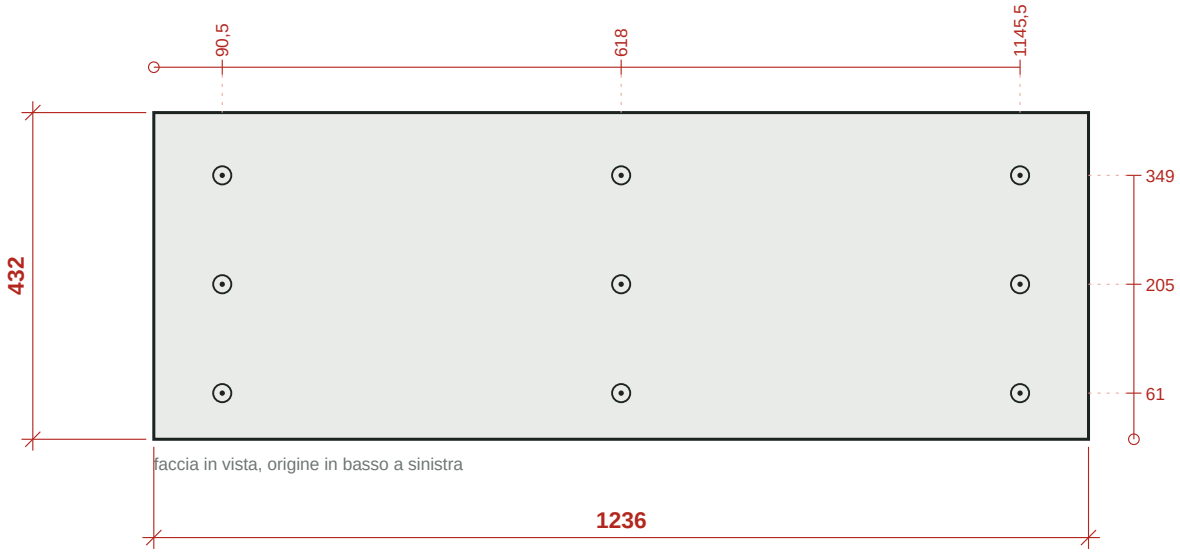


POSIZIONE

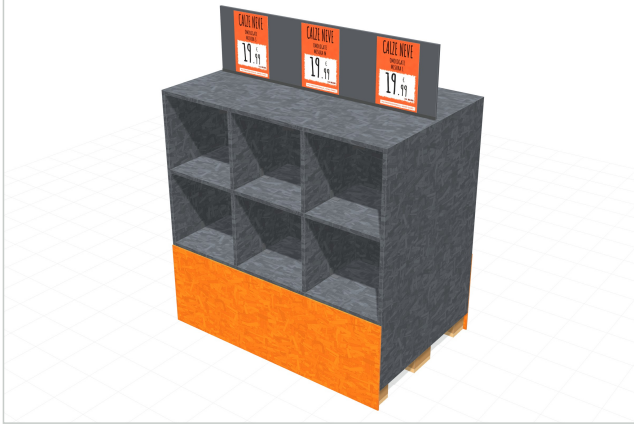

## × 2

pezzi uguali da tagliare

| | |
|---|---|
| Dimensioni | **1236 × 432 mm** |
| Spessore | **6 mm** |
| Materiale | **OSB di pioppo 6 mm, verniciato antracite** |
| Superficie | **0,534 m² cad. · 1,068 m² tot.** |

**FORI**

⊙ 9 × Ø3,5 passante, svasato · vite 3,5 × 30

Le viti entrano nei blocchi dei pallet e li legano tra loro. Copre anche i bordi dei fianchi.

**ESPOSITORE CALZE NEVE**


Tavola 8 di 10 · scala 1:10 · quote in mm

3 pallet EPAL · scaffale 800 / 2 livelli · 29/10/2026

# H Foglio insegna

1200 × 320 × 10 mm · Forex 10 mm grigio antracite

POSIZIONE

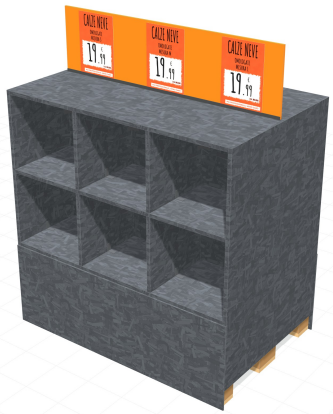





**× 1**

pezzo da tagliare

| | |
|---|---|
| Dimensioni | **1200 × 320 mm** |
| Spessore | **10 mm** |
| Materiale | **Forex 10 mm grigio antracite** |
| Superficie | **0,384 m² cad. · 0,384 m² tot.** |

Senza fori: si infila nel profilo a U. I 5 cartelli A4 vanno a 1 cm dal bordo alto, sopra i rispettivi vani.

**ESPOSITORE CALZE NEVE**

Tavola 9 di 10 · scala 1:10 · quote in mm

3 pallet EPAL · scaffale 800 / 2 livelli · 29/10/2026

# Sequenza di montaggio

Attrezzi: avvitatore, punta a gradino per confirmat (Ø5/Ø7), punte Ø2,5 e Ø4 con svasatore, metro, squadra, 2 morsetti.

1. Impila i 3 pallet allineati.
2. Appoggia il fondo 1200 × 800 sul pallet in alto e avvitalo alle tavole del pallet. Servono: 8 viti 4 × 50.
3. Livello 1: metti in piedi spina centrale e 3 divisori, fissali al ripiano e tra loro con le squadrette. Servono: 17 squadrette, 68 viti 3,5 × 16.
4. Appoggia il ripiano 2: fissa le squadrette in testa a spina e divisori e avvita dall'alto i confirmat nelle teste. Servono: 11 squadrette, 44 viti 3,5 × 16, 10 confirmat 7 × 50.
5. Livello 2: metti in piedi spina centrale e 3 divisori, fissali al ripiano e tra loro con le squadrette. Servono: 17 squadrette, 68 viti 3,5 × 16.
6. Chiudi con il piano superiore: squadrette in testa a spina e divisori, confirmat dall'alto nelle teste. Servono: 11 squadrette, 44 viti 3,5 × 16, 10 confirmat 7 × 50.
7. Monta i due fianchi: confirmat nei bordi di ripiani e piano, viti nelle traverse dei pallet, squadrette negli angoli interni. Si fermano a 100 da terra, sopra le aperture forche. Servono: 20 squadrette, 80 viti 3,5 × 16, 18 confirmat 7 × 50, 18 viti 4 × 50.
8. Avvita i pannelli da 6 mm sui lati lunghi, nei blocchi di ogni pallet: coprono i bordi dei fianchi e legano i pallet tra loro. Servono: 18 viti 3,5 × 30.
9. Avvita il profilo a U sul piano superiore, infila il foglio e attacca i 5 cartelli prezzo A4: S, M, L sul fronte, XL e XXL sul retro, ognuno sopra il suo vano. Servono: 4 viti 3,5 × 20.

Consigli: preforare con punta Ø2,5 tutte le viti delle squadrette per non aprire il bordo del pannello. Montare a vista libera dalla spina verso l'esterno; i fianchi per ultimi tengono in squadra tutto il corpo. Nel configuratore, il montaggio passo-passo mostra ogni vite fuori dal foro con la linea fino al punto d'ingresso.